



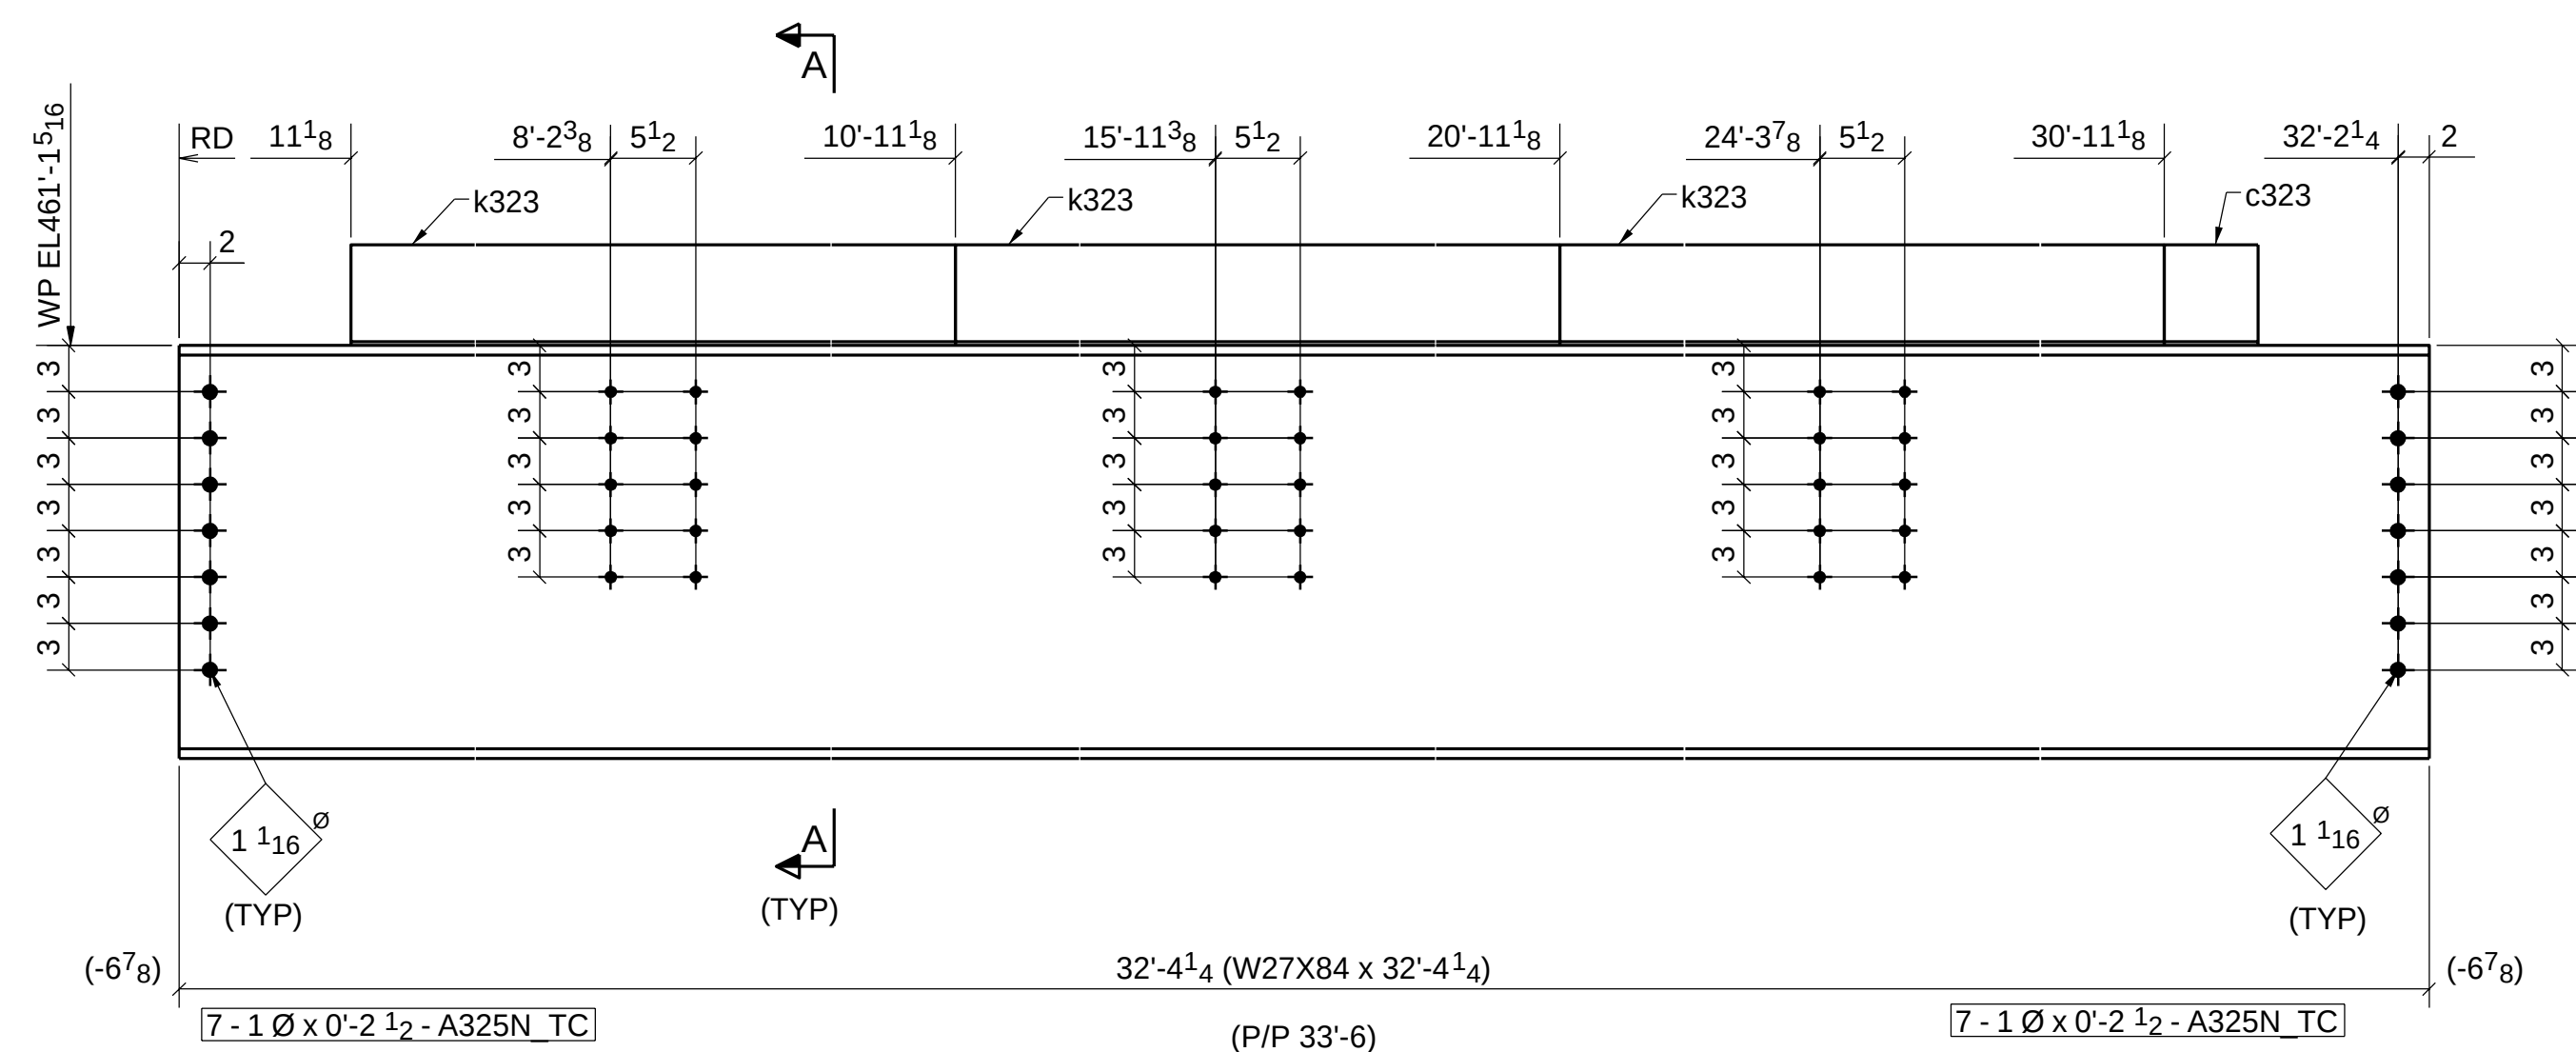


ONE ~ BEAM ~ 323B1
(ONE @ E302)
(NO PAINT)

W	26 3/4 x 7/16
F	10 x 5/8

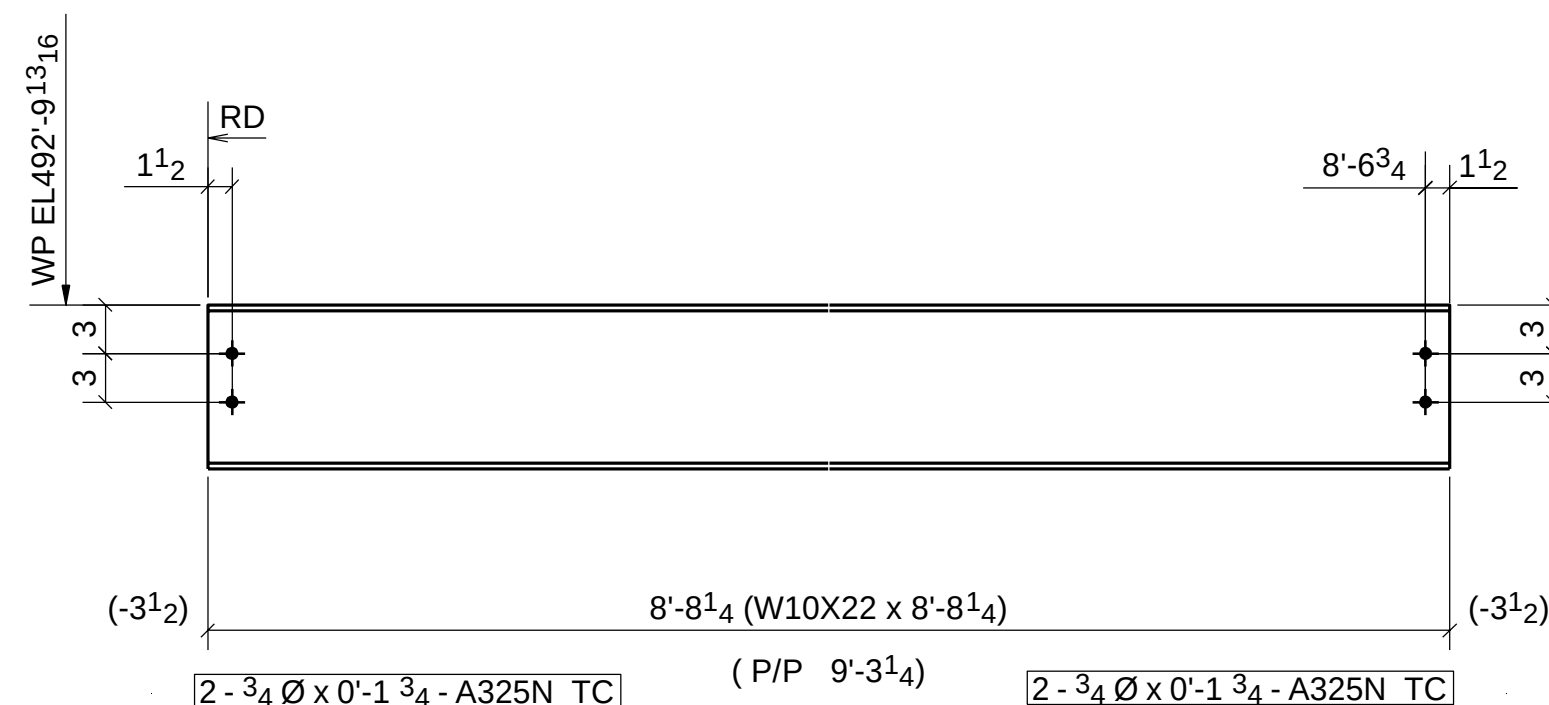


ONE ~ BEAM ~ 323B2
(ONE @ E307)
(NO PAINT)

W	10 1/8 x 1/4
F	5 3/4 x 3/8

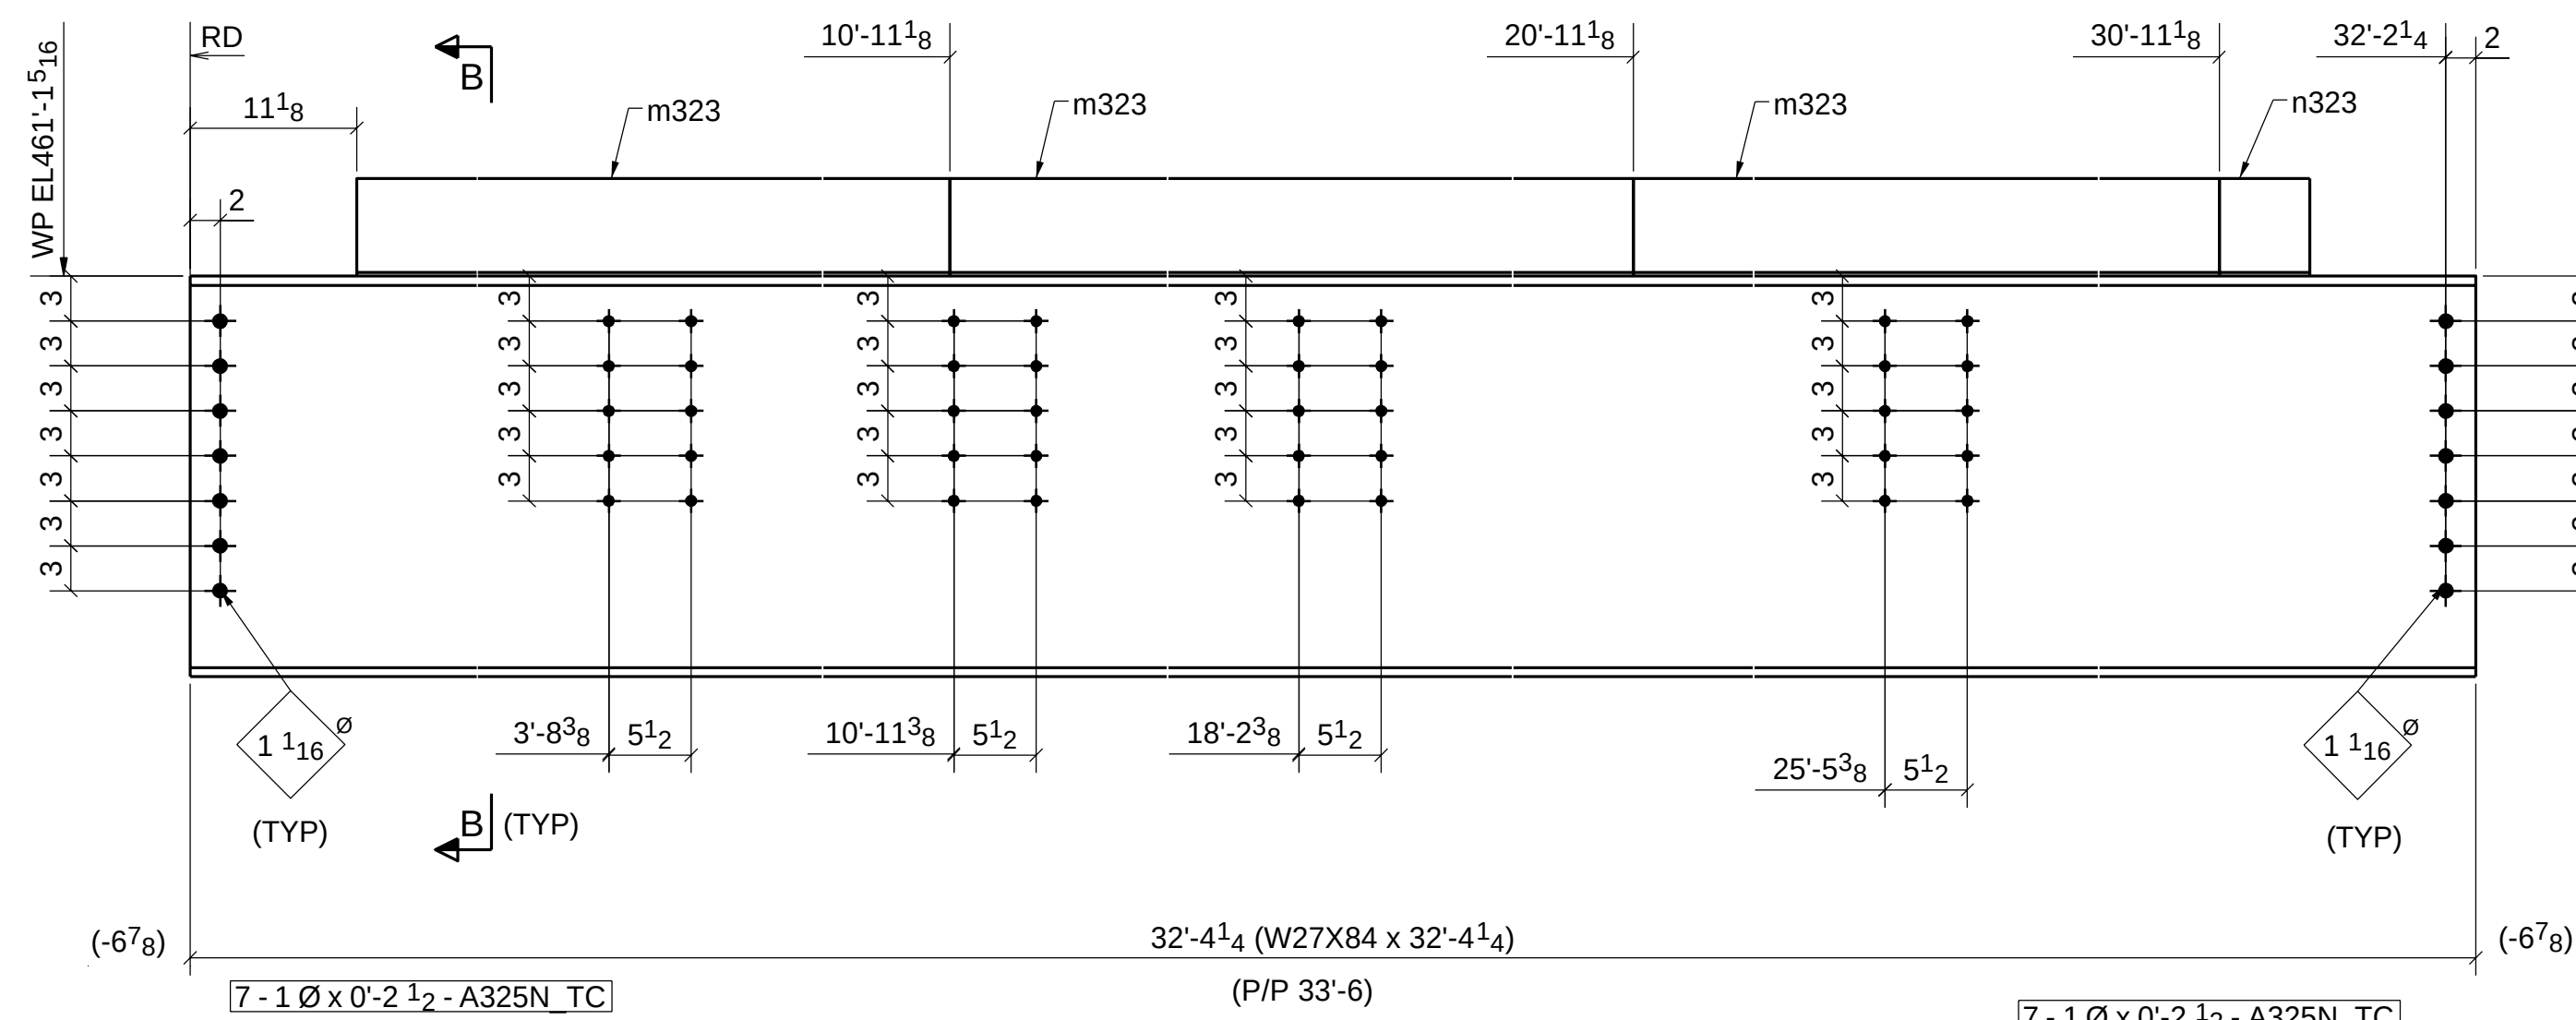


ONE ~ BEAM ~ 323B3
(ONE @ E302)
(NO PAINT)

W	26 3/4 x 7/16
F	10 x 5/8

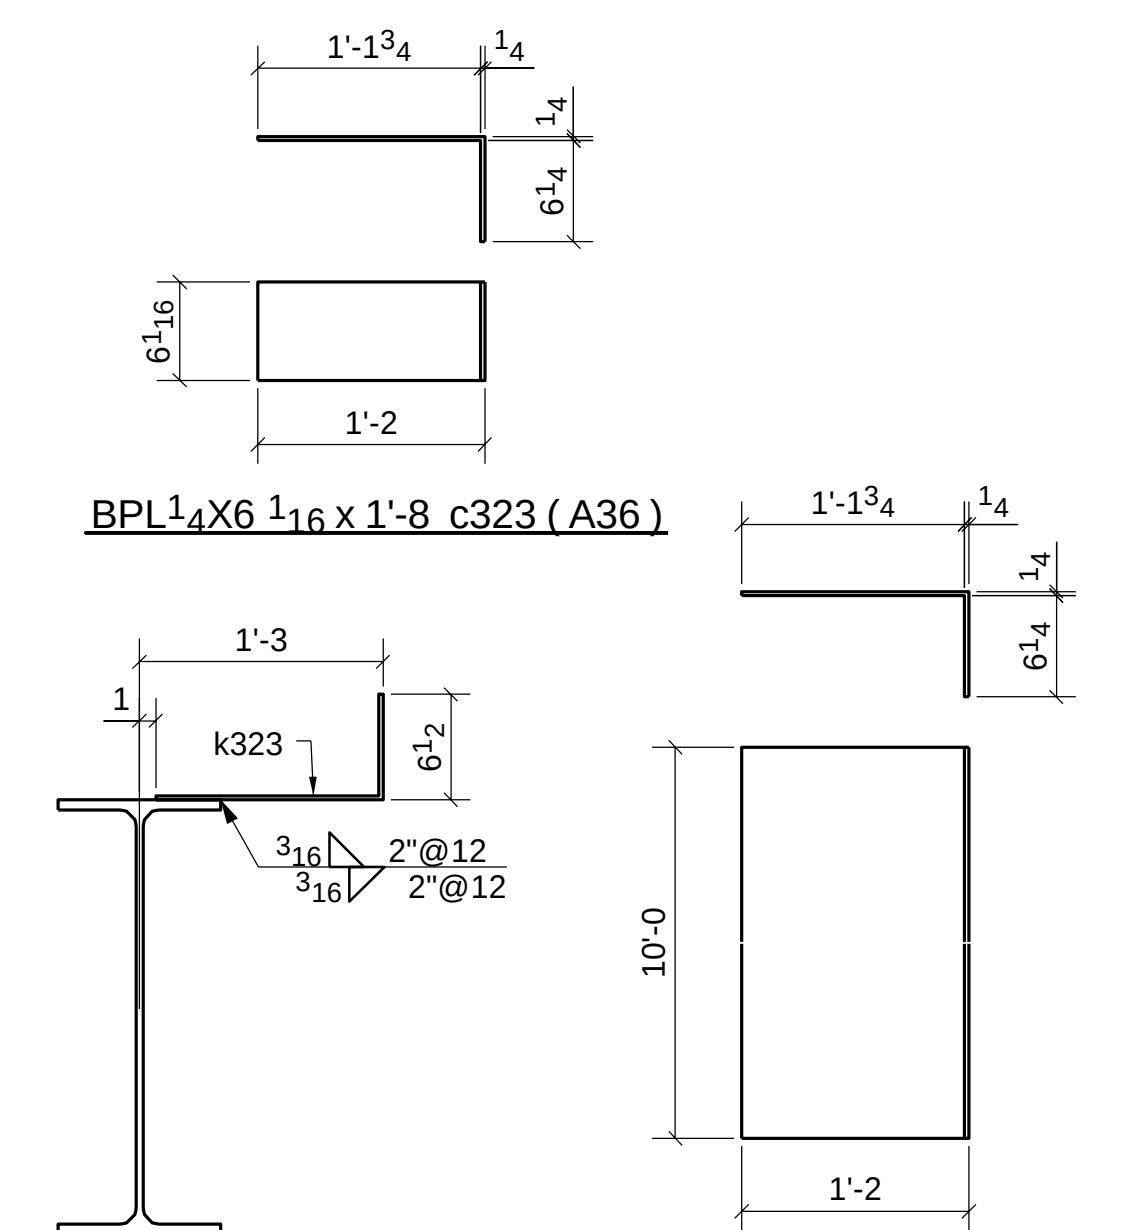

SECTION A - A

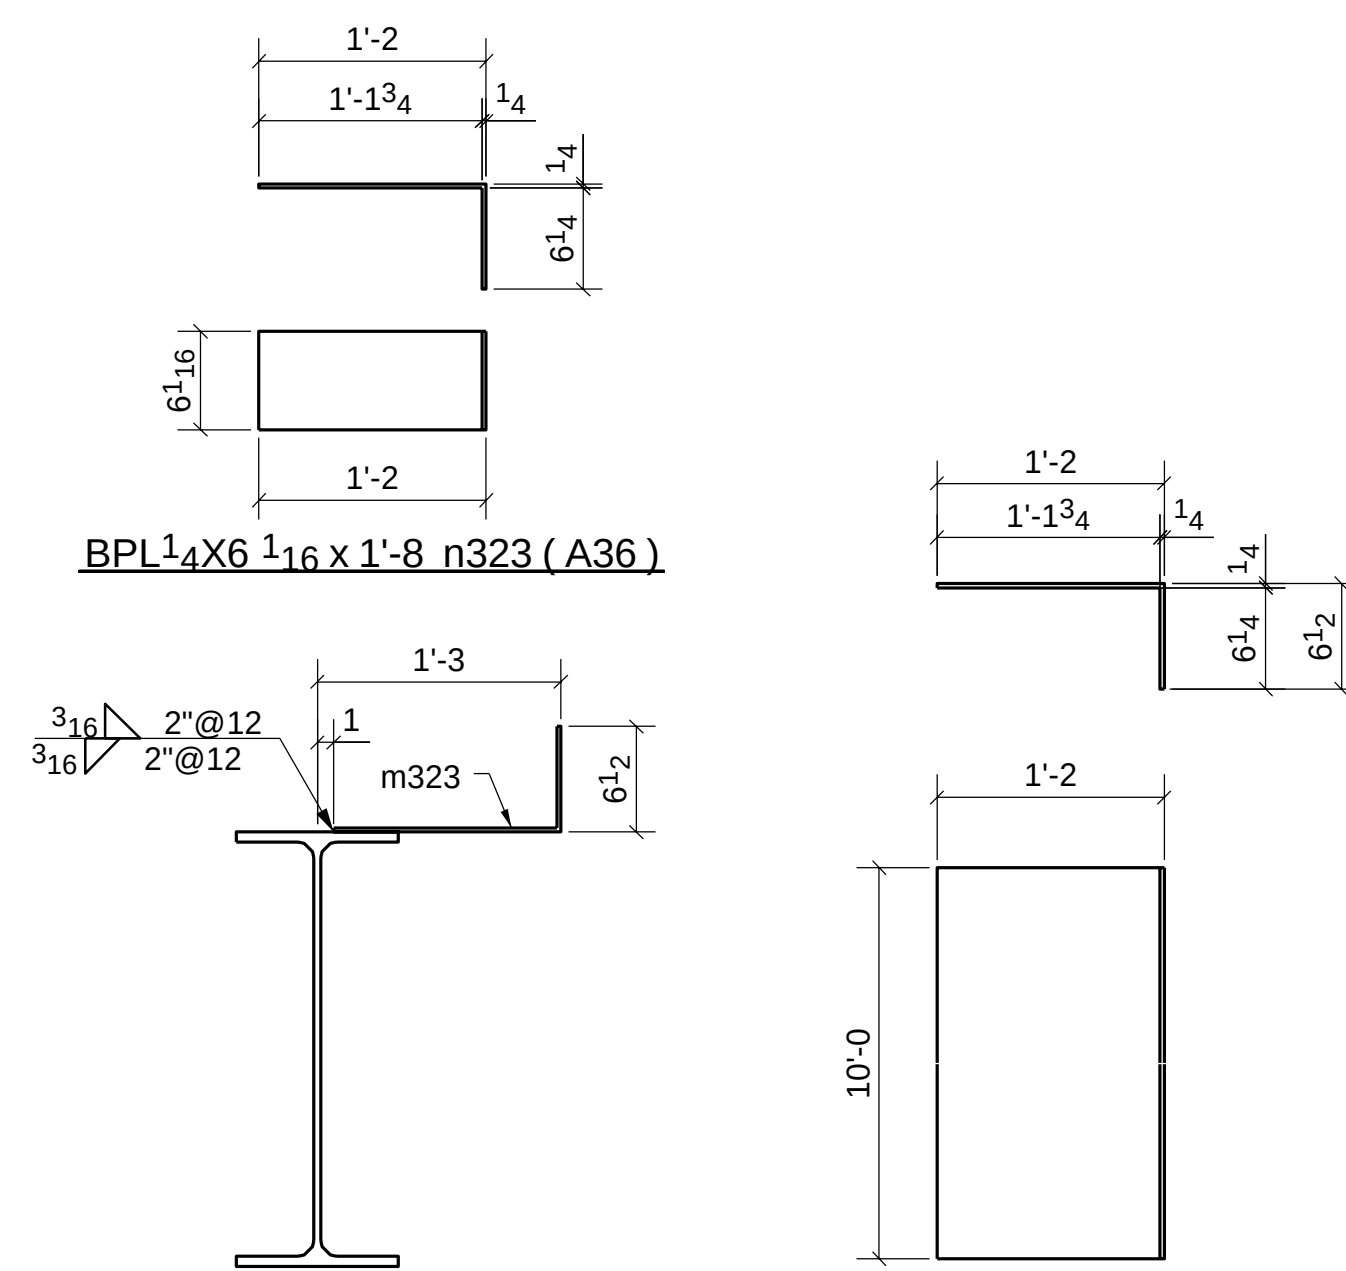

SECTION B - B



FOR CONSTRUCTION

CONSTRUCTION ISSUE					APPROVAL ISSUE				
0	For Constructions	LAK	10/13/17	A	For Approval			AMJ	08/18/17
REV. NO.	DESCRIPTION	MADE	DATE	REV. NO.	DESCRIPTION			MADE	DATE

[illegible]

WEEDY

LAUDER

NOTE: UNLESS OTHERWISE SPECIFIED, ALL WELDING TO BE PERFORMED IN ACCORDANCE WITH AWS D1.1 WITH E7XXX LH FILLER METAL

NOTE * IMPORTANT * NOTE

We will not accept charges for labor, materials, or corrective work unless duly authorized.

JOB#		11085	
SHEET#		323	
REV.#			
CUSTOMER	DRAWN BY	DATE	SURFACE PREP: SSPC-SP2 / SP3 FINISH: NO PAINT
PROJECT	CHECKED BY	DATE	
LOCATION	REVISED BY	DATE	
SHOP NOTES 13/16 U.N. HICLES: E70XX 3) WELDS 2) MATERIAL SPEC			