

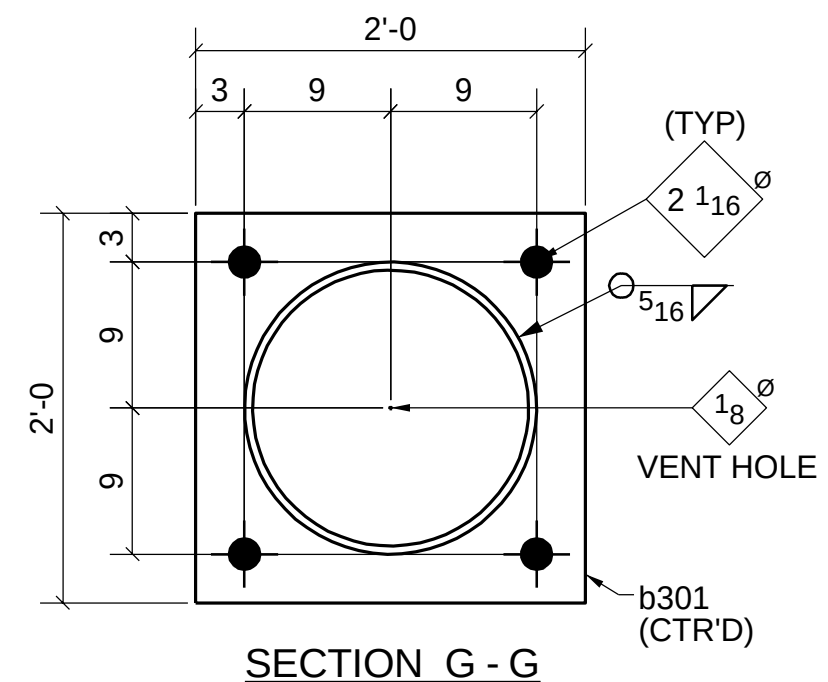


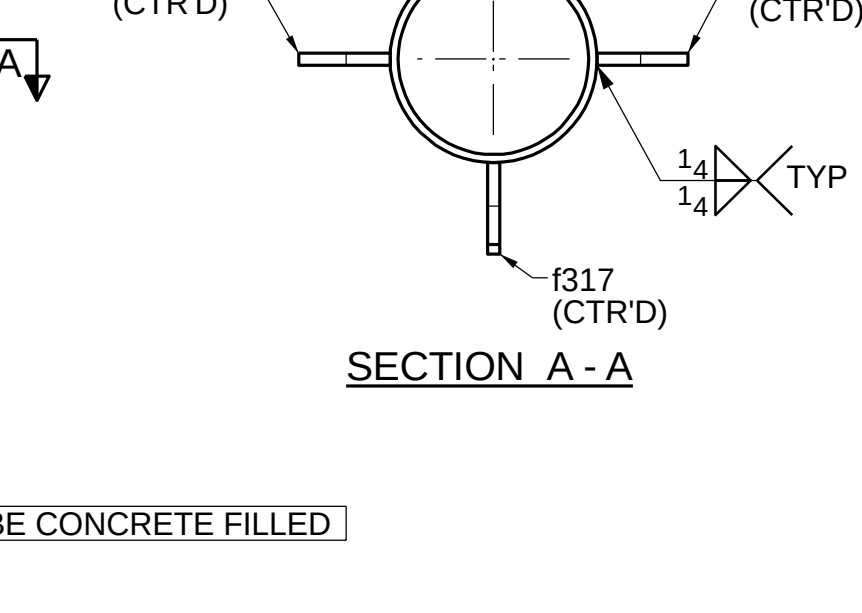

COLUMN SHALL BE CONCRETE FILLED

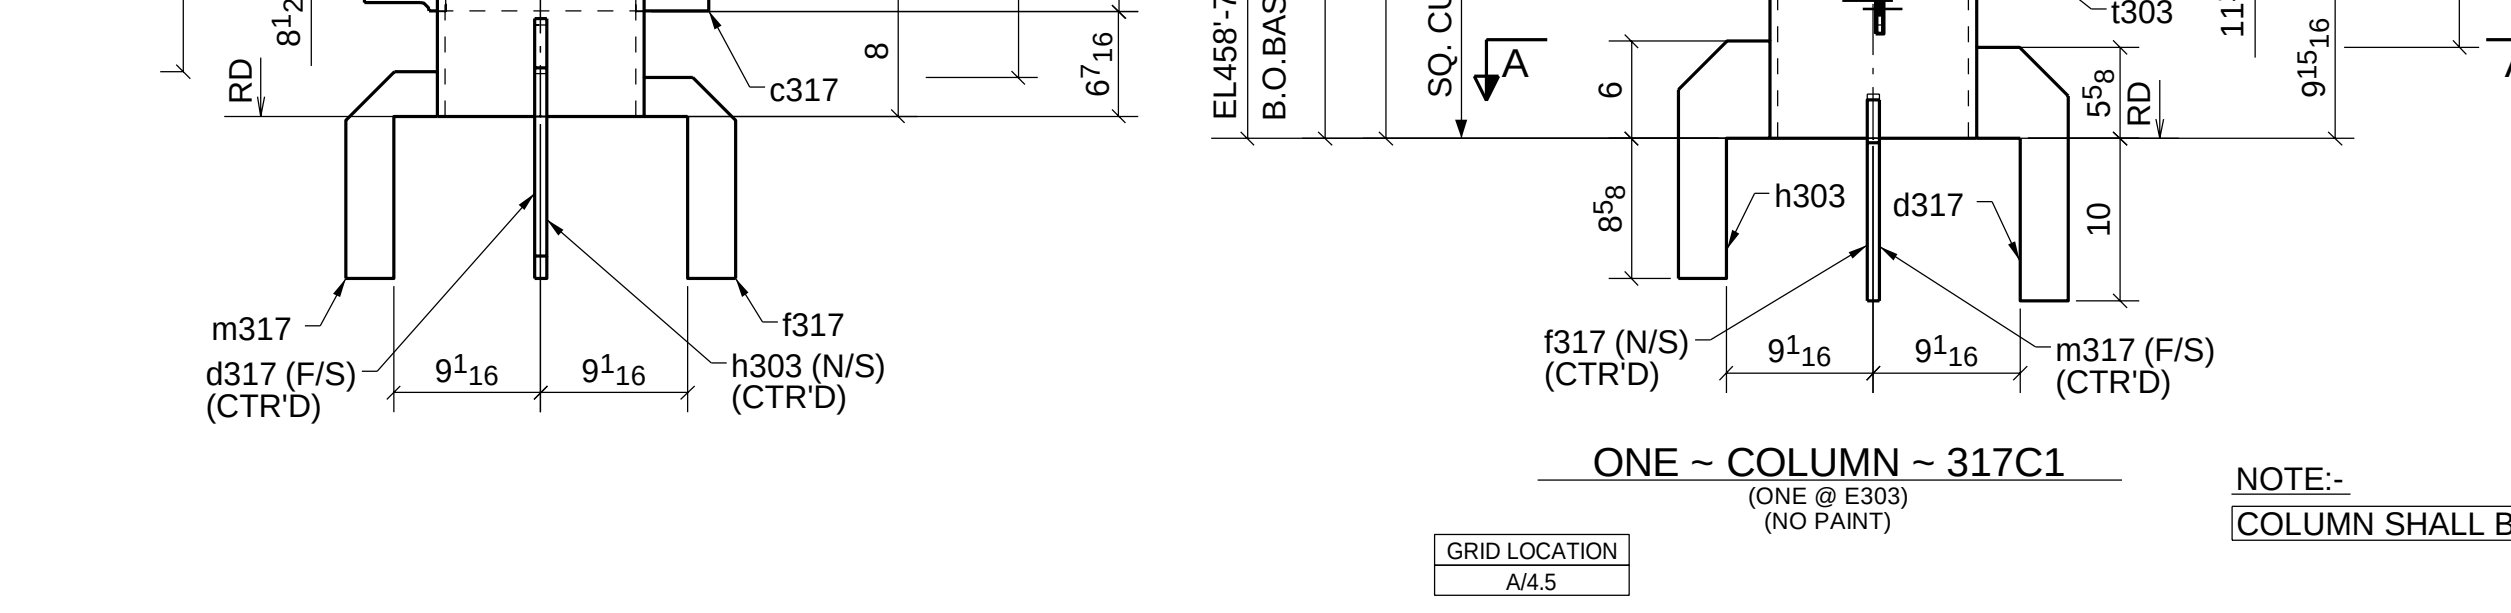

CONSTRUCTION ISSUE				APPROVAL ISSUE			
0	For Constructions	A/J1	10/13/17	A	For Approval	A/J1	08/18/17
REV. NO.	DESCRIPTION	MADE	DATE	REV. NO.	DESCRIPTION	MADE	DATE

WEEDY				LAUDER			
NOTE: UNLESS OTHERWISE SPECIFIED, ALL WELDING TO BE PERFORMED IN ACCORDANCE WITH AWS D1.1 WITH E7XXX LH FILLER METAL							
NOTE * IMPORTANT * NOTE We will not accept charges for labor, materials, or corrective work unless duly authorized.							
ISSUE			APPROVAL				
AJI	10/13/17	A	For Approval			AJI	08/18/17
MADE	DATE	REV. NO.	DESCRIPTION			MADE	DATE

SHEET#

1108
31

 $\wedge_0$