

H

G

F









E

D

C

B

A

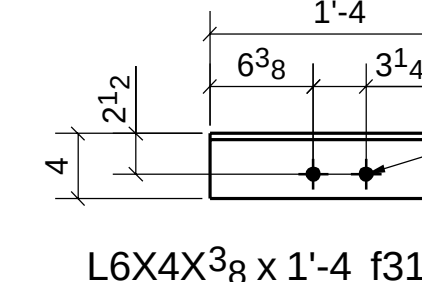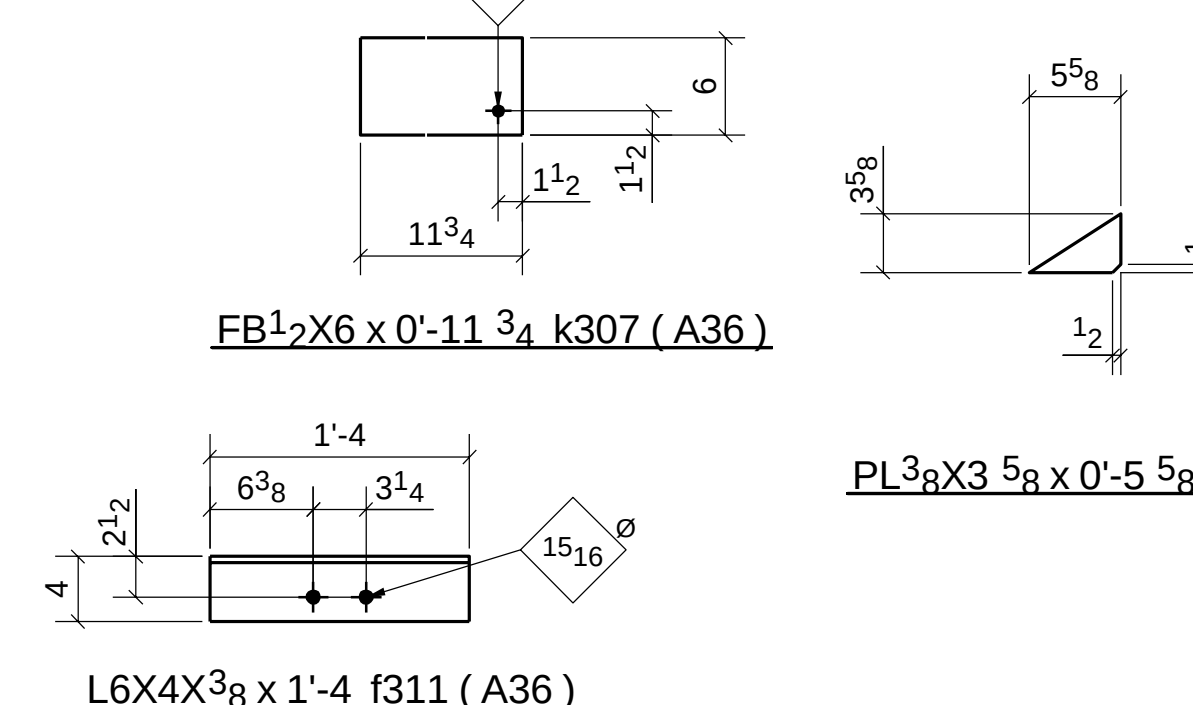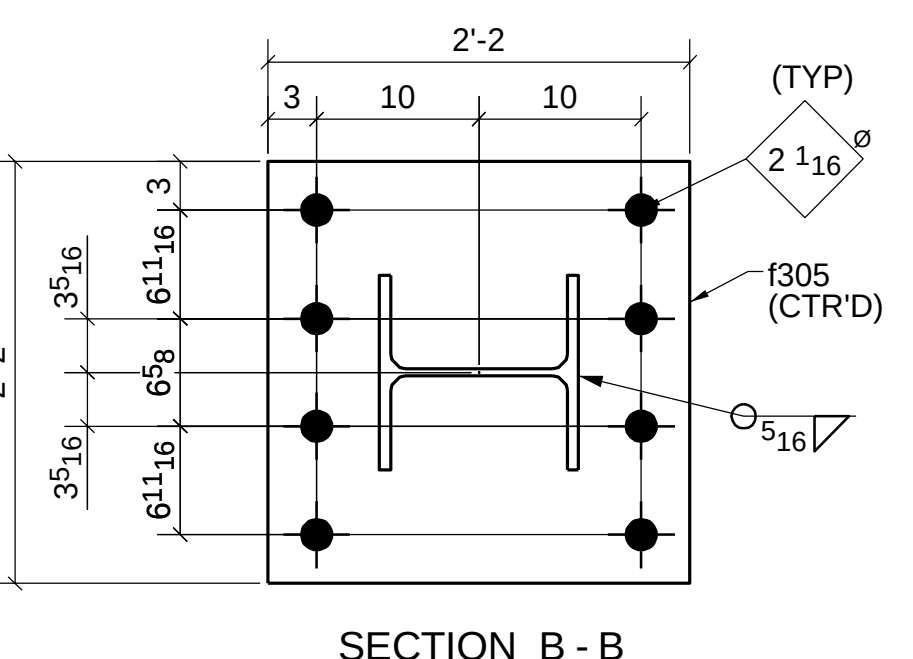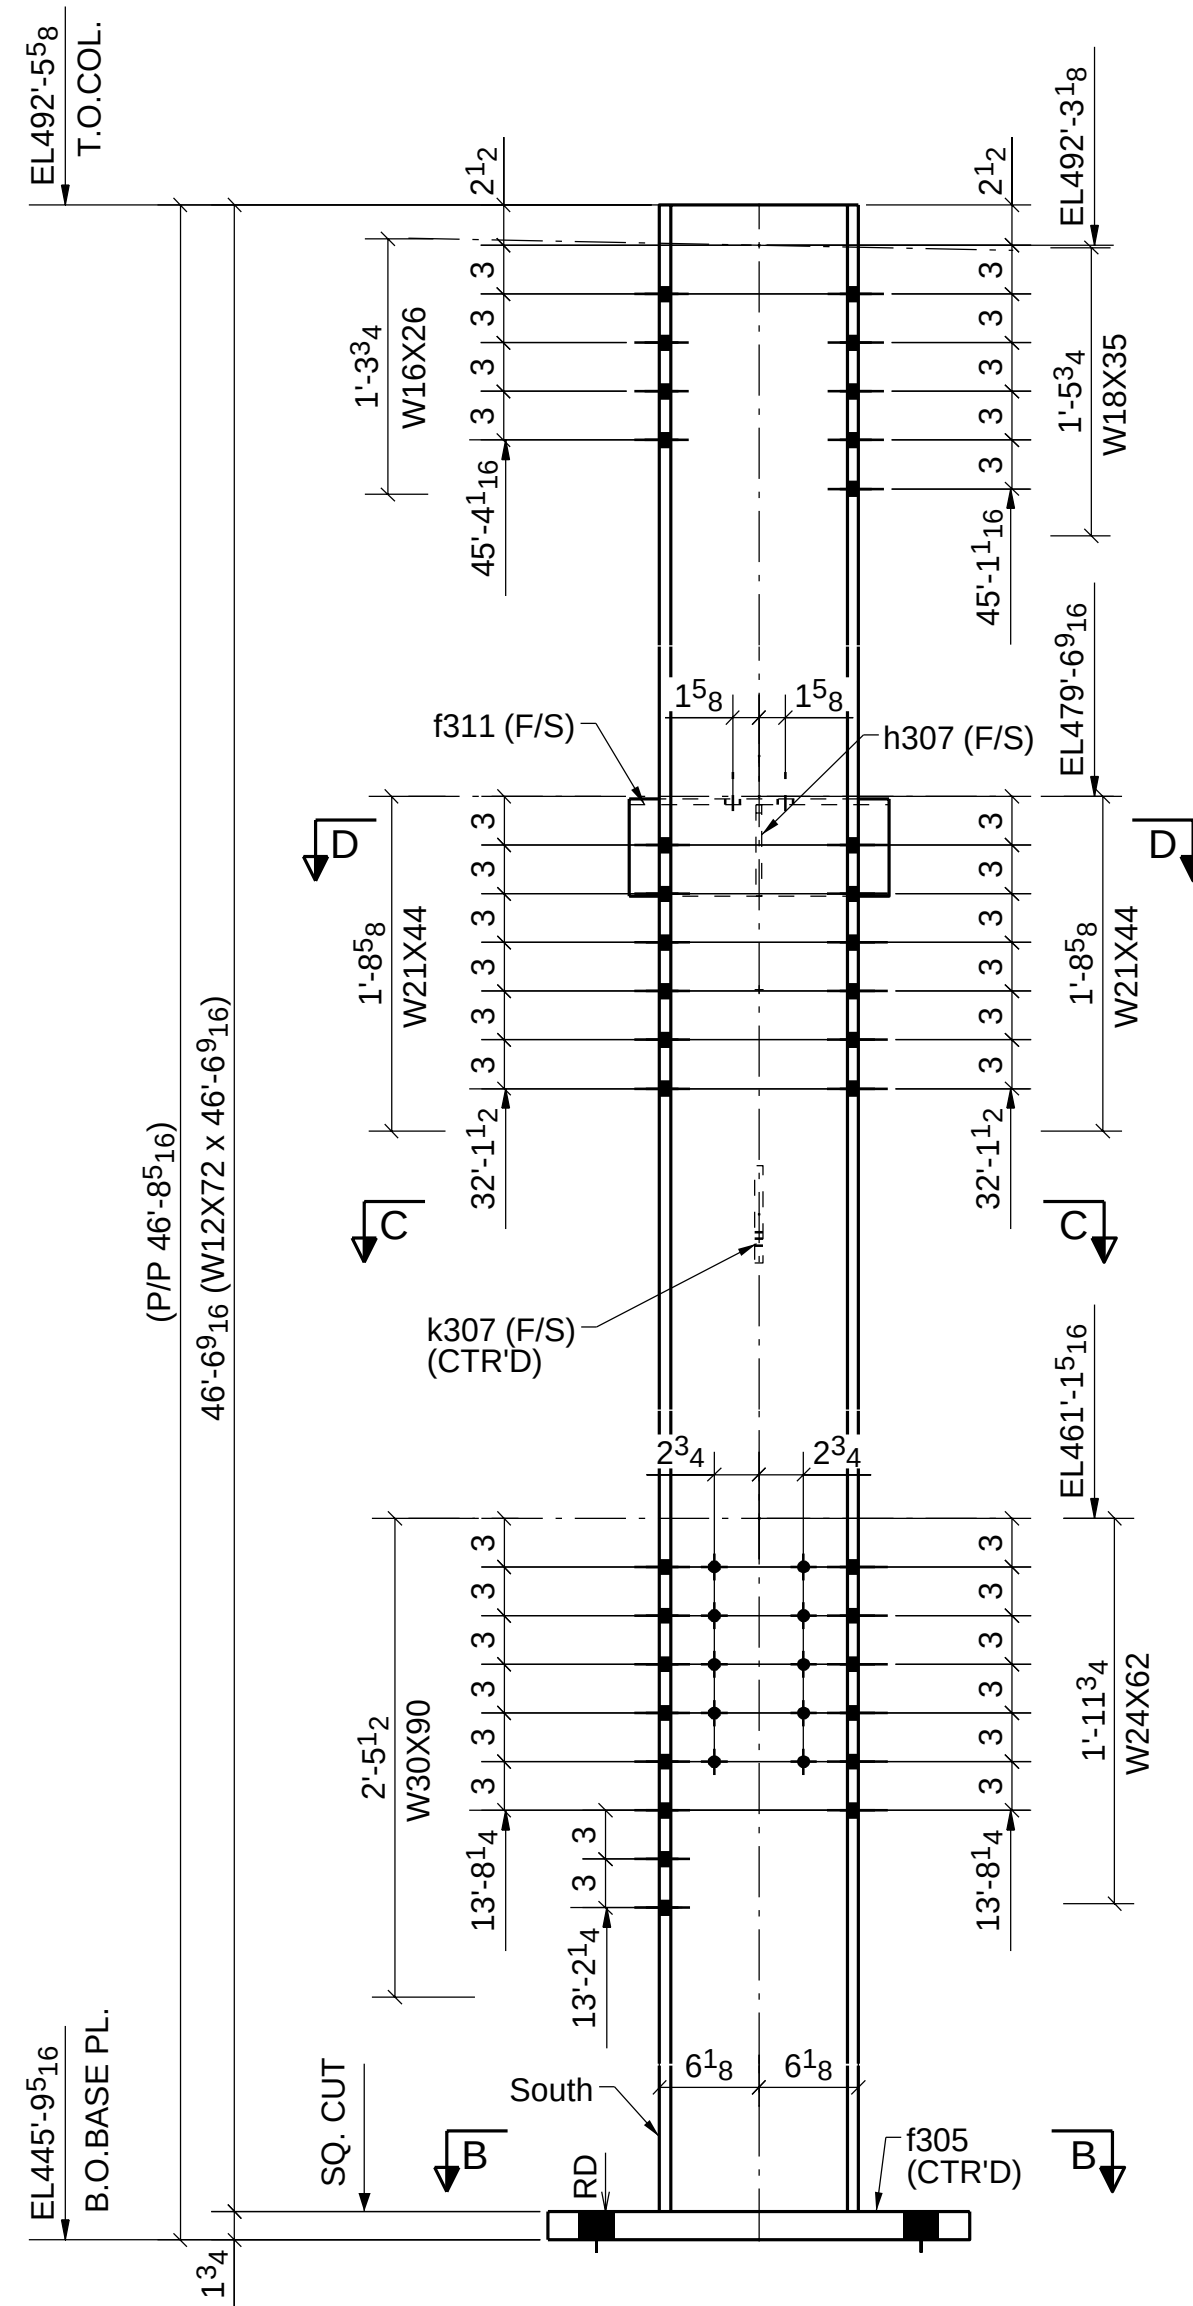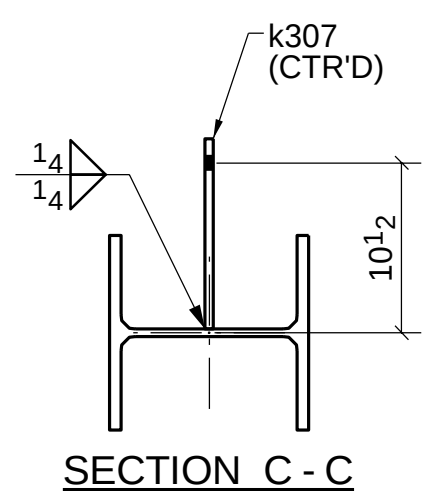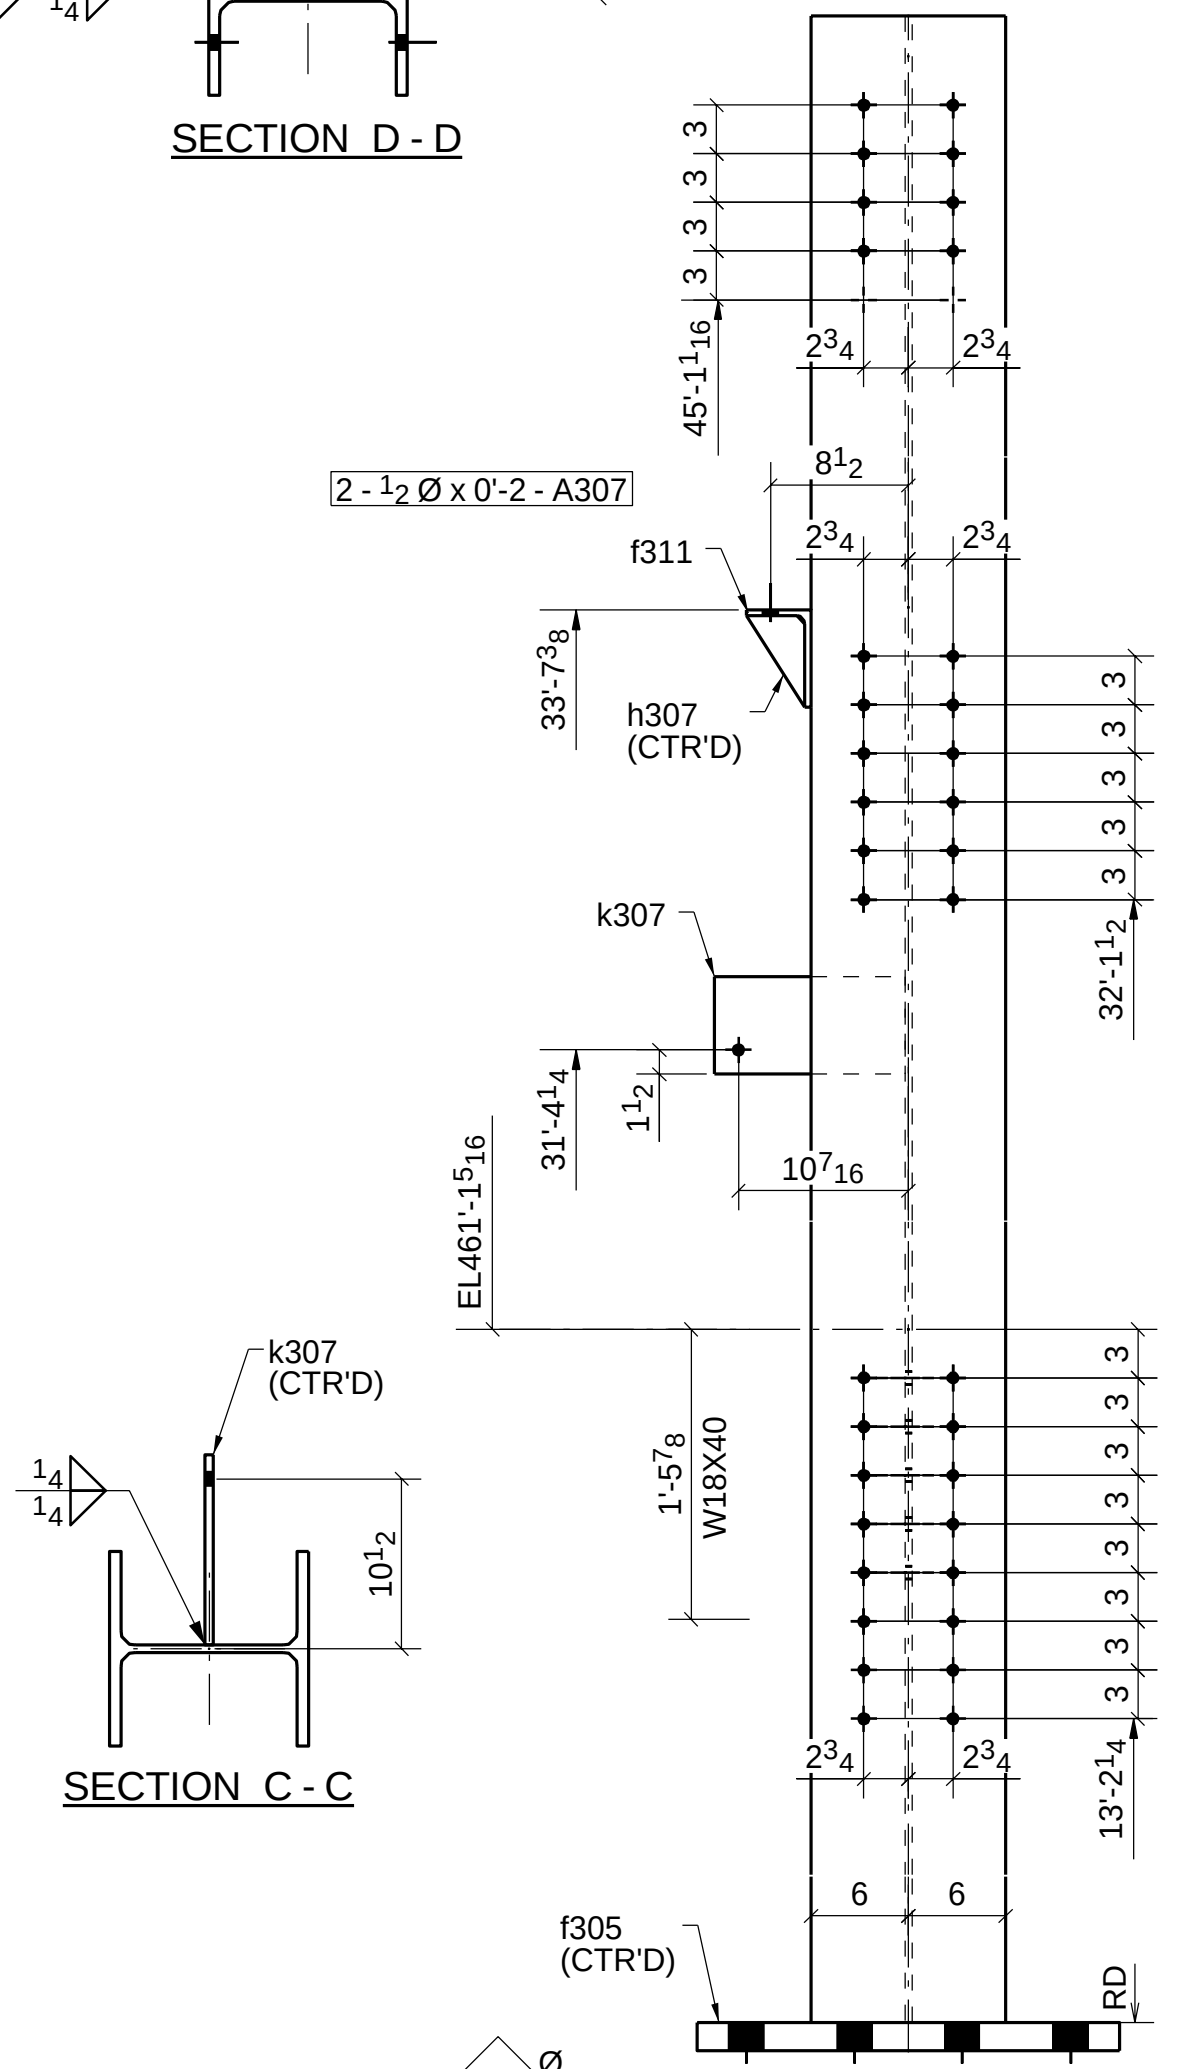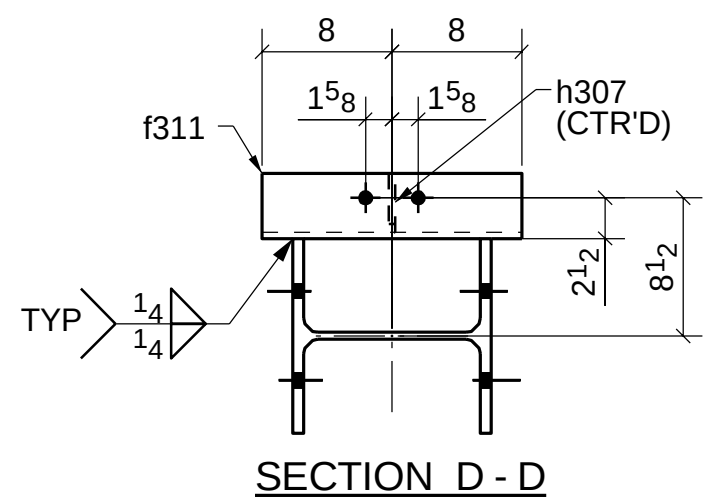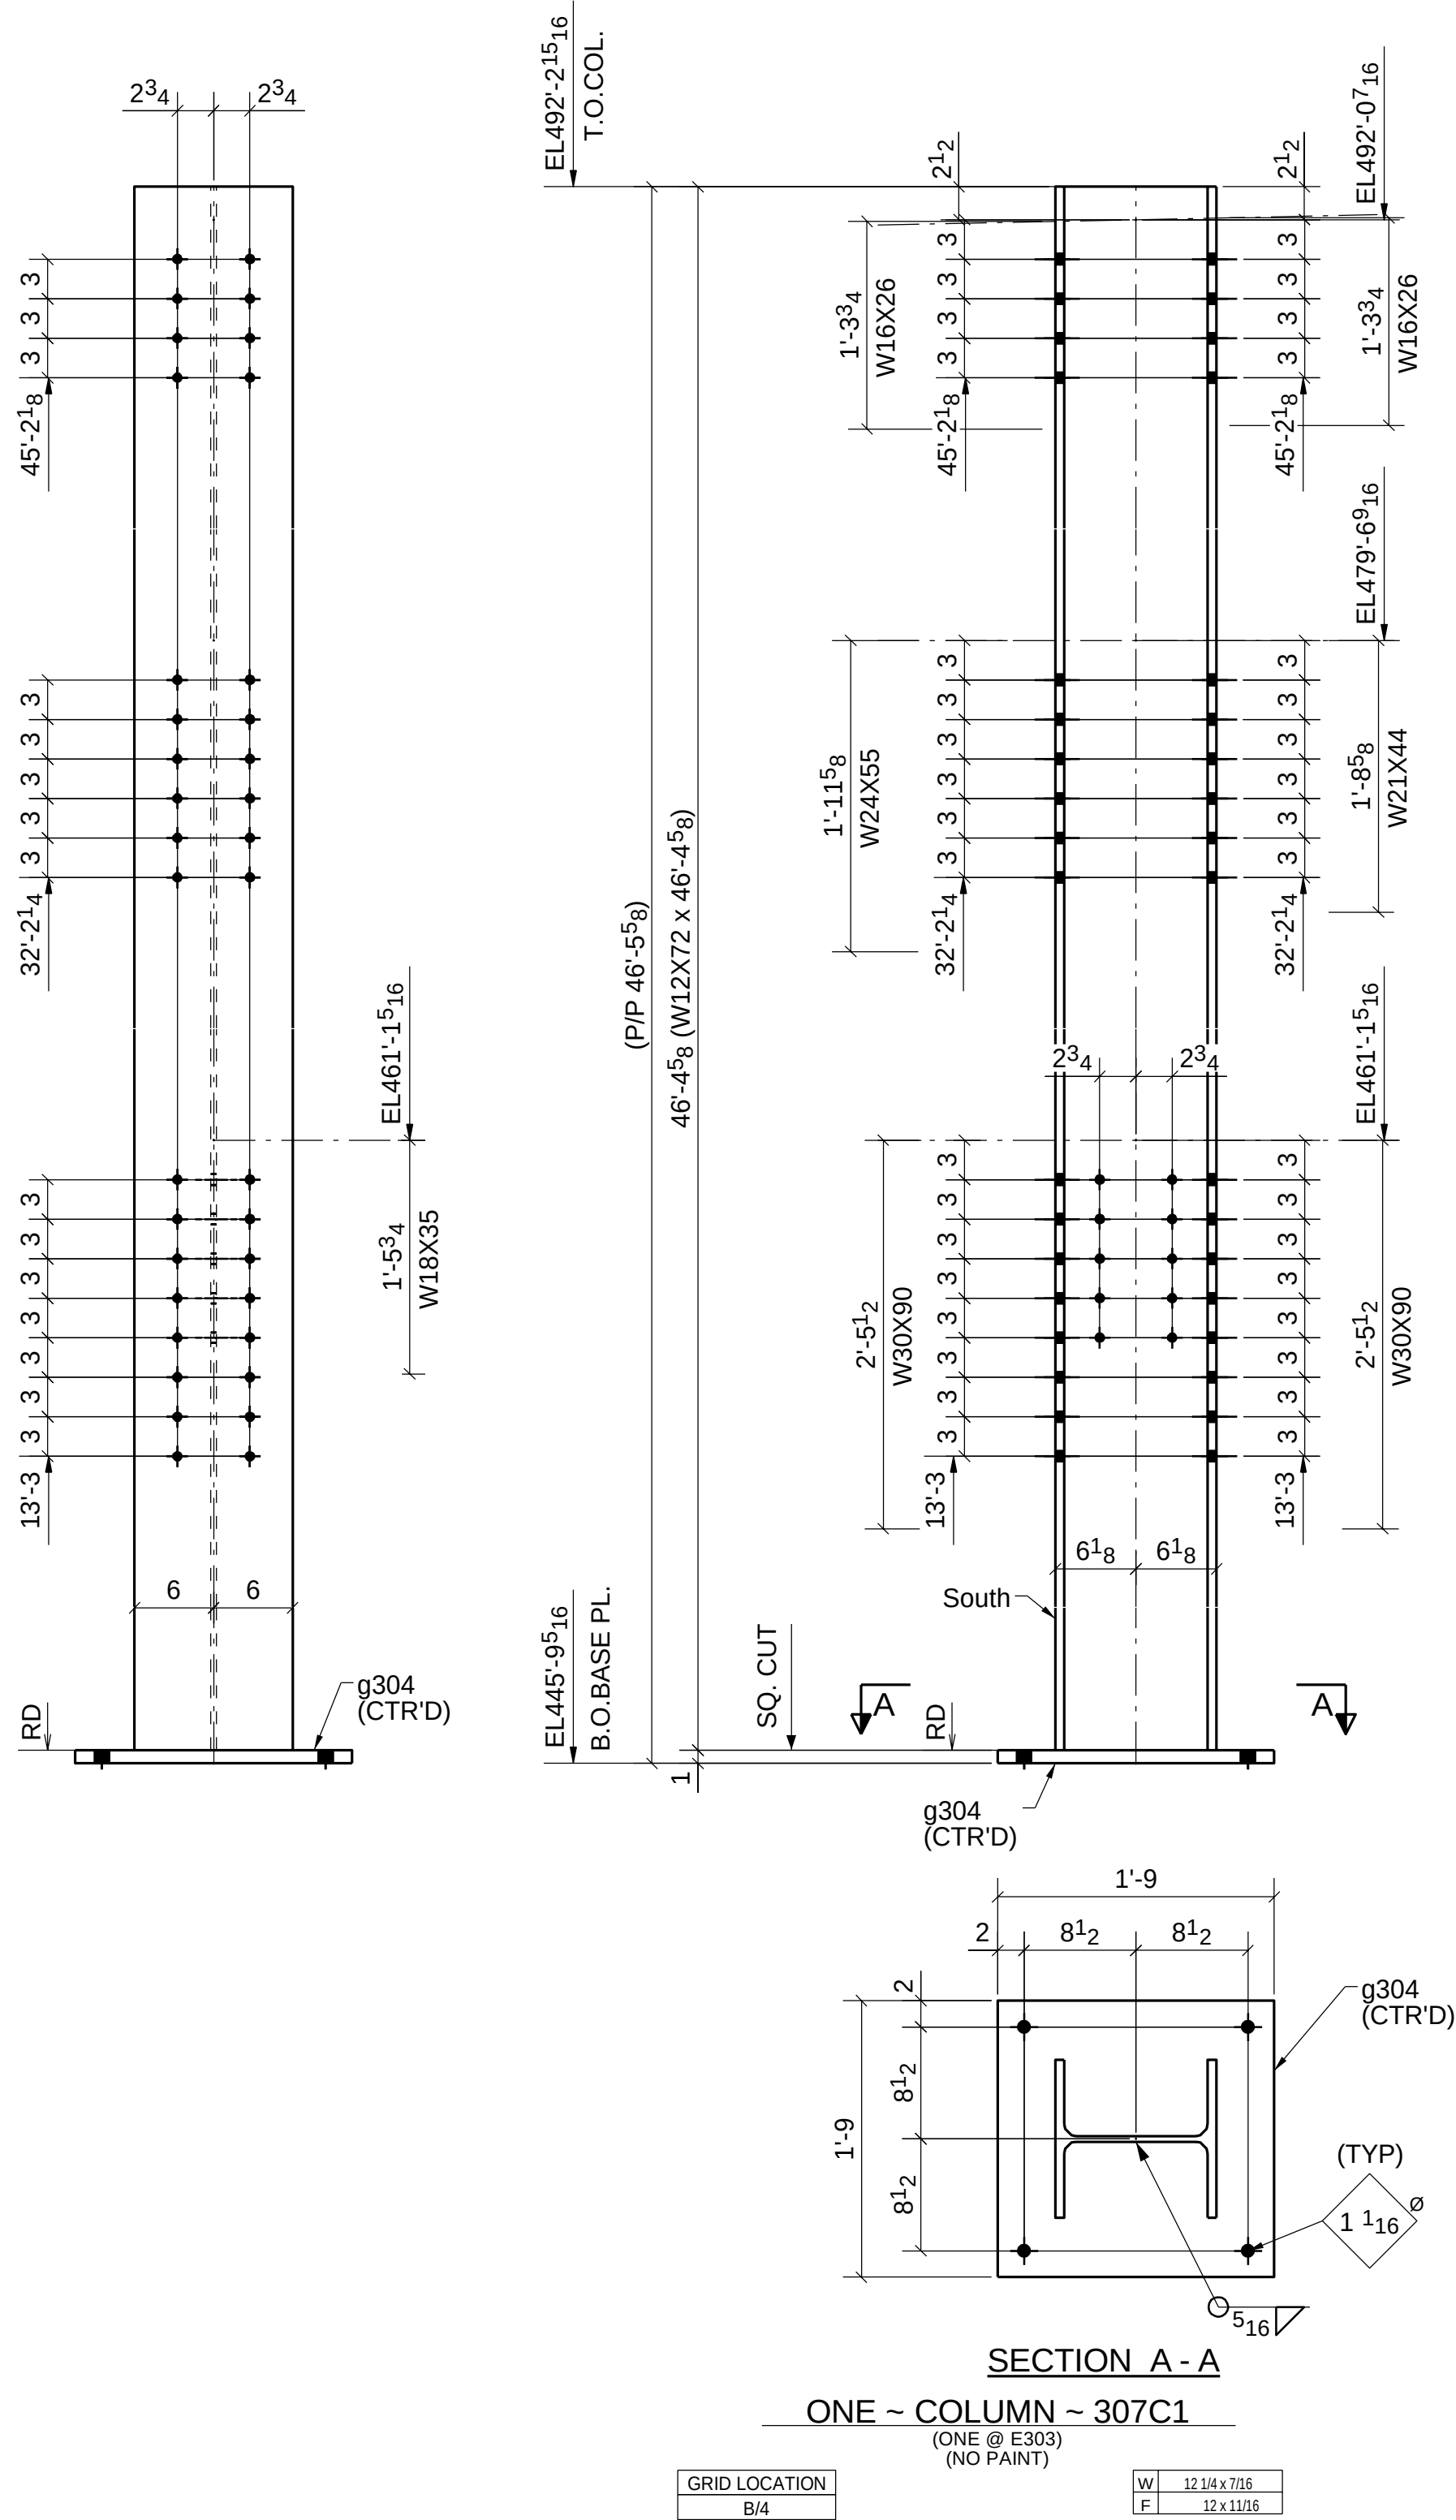

ONE ~ COLUMN ~ 307C2
(ONE @ E302)
(NO PAINT)

GRID LOCATION
B/3

W 12 1/4 x 71/8
F 12 x 11/8

AISC CERTIFIED
FABRICATOR



FOR CONSTRUCTION

CONSTRUCTION ISSUE				APPROVAL ISSUE			
0	For Construction	AJI	10/13/17	A	For Approval	AJI	08/18/17
REV. NO.	DESCRIPTION	MADE	DATE	REV. NO.	DESCRIPTION	MADE	DATE

BILL OF MATERIALS						
MARK	QTY.	MATERIALS	LENGTH	PHASE	REMARKS	MATERIAL
307C1	1	COLUMN		3		
307C1	1	W12X72	46'-4 5/8"			A992
g304	1	PL1X21	1'-9"			A36
307C2	1	COLUMN		3		
307C2	1	W12X72	46'-6 9/16"			A992
f305	1	PL1 3/4X26	2'-2"			A36
f311	1	L6X4X3/8	1'-4"			A36
h307	1	PL3/8X3 5/8	0'-5 5/8"			A36
k307	1	FB1/2X6	0'-11 3/4"			A36

